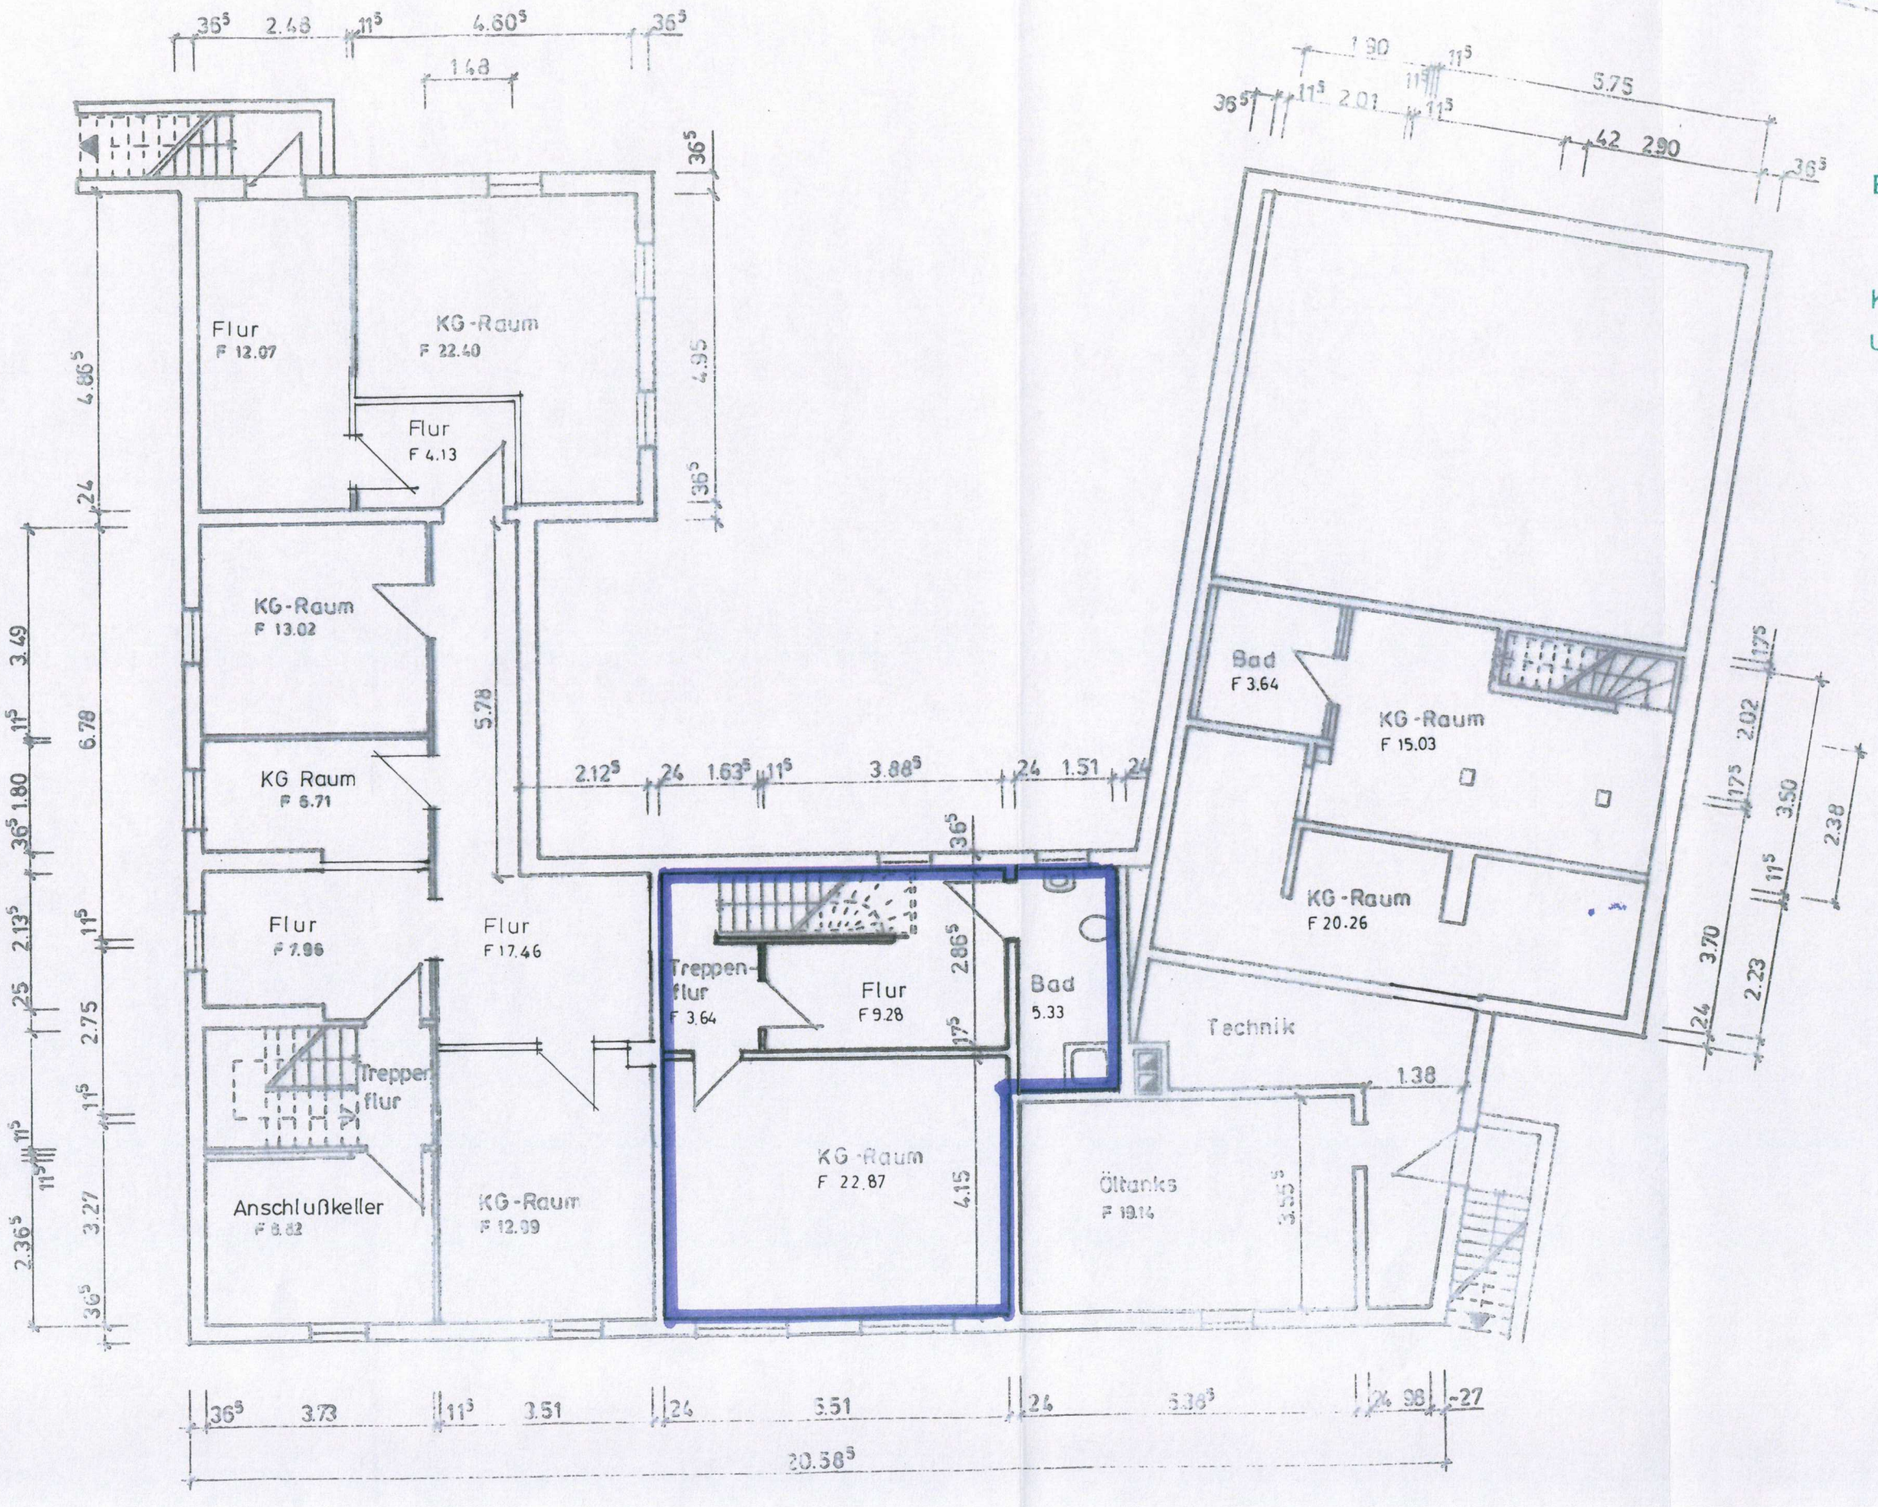


Bestandteil des Bescheides

0704/03/95

Kreis Rendsburg-Eckernförde
- Der Landrat -
Untere Bauaufsichtsbehörde

B.-NR.: 15/652 Z.-NR.: 3/1
DARSTELLUNG: KG-Grundriss
MA: 1:100 GEZ: wie.
DAT: 11.09.2015 GEÄ: -

BAUVORHABEN: Nutzungsänderung
BAUORT: Wilhelm-Stabe-Str. 4, 24582 Wattenbek
BAUHERR: Rolf Schwarten
DER BAUHERR:
DER BAUVORLAGEBERECHTIGTE:

ARCHITEKTURBÜRO LADWIG Ralf Dieter Ladwig Architekt Dipl.-Ing. Heintzestr. 32, 24582 Bordesholm Tel.: 0 43 22 - 75 78-0 / Fax: 75 78-88

WOHNUNG A =
WOHNUNG B =