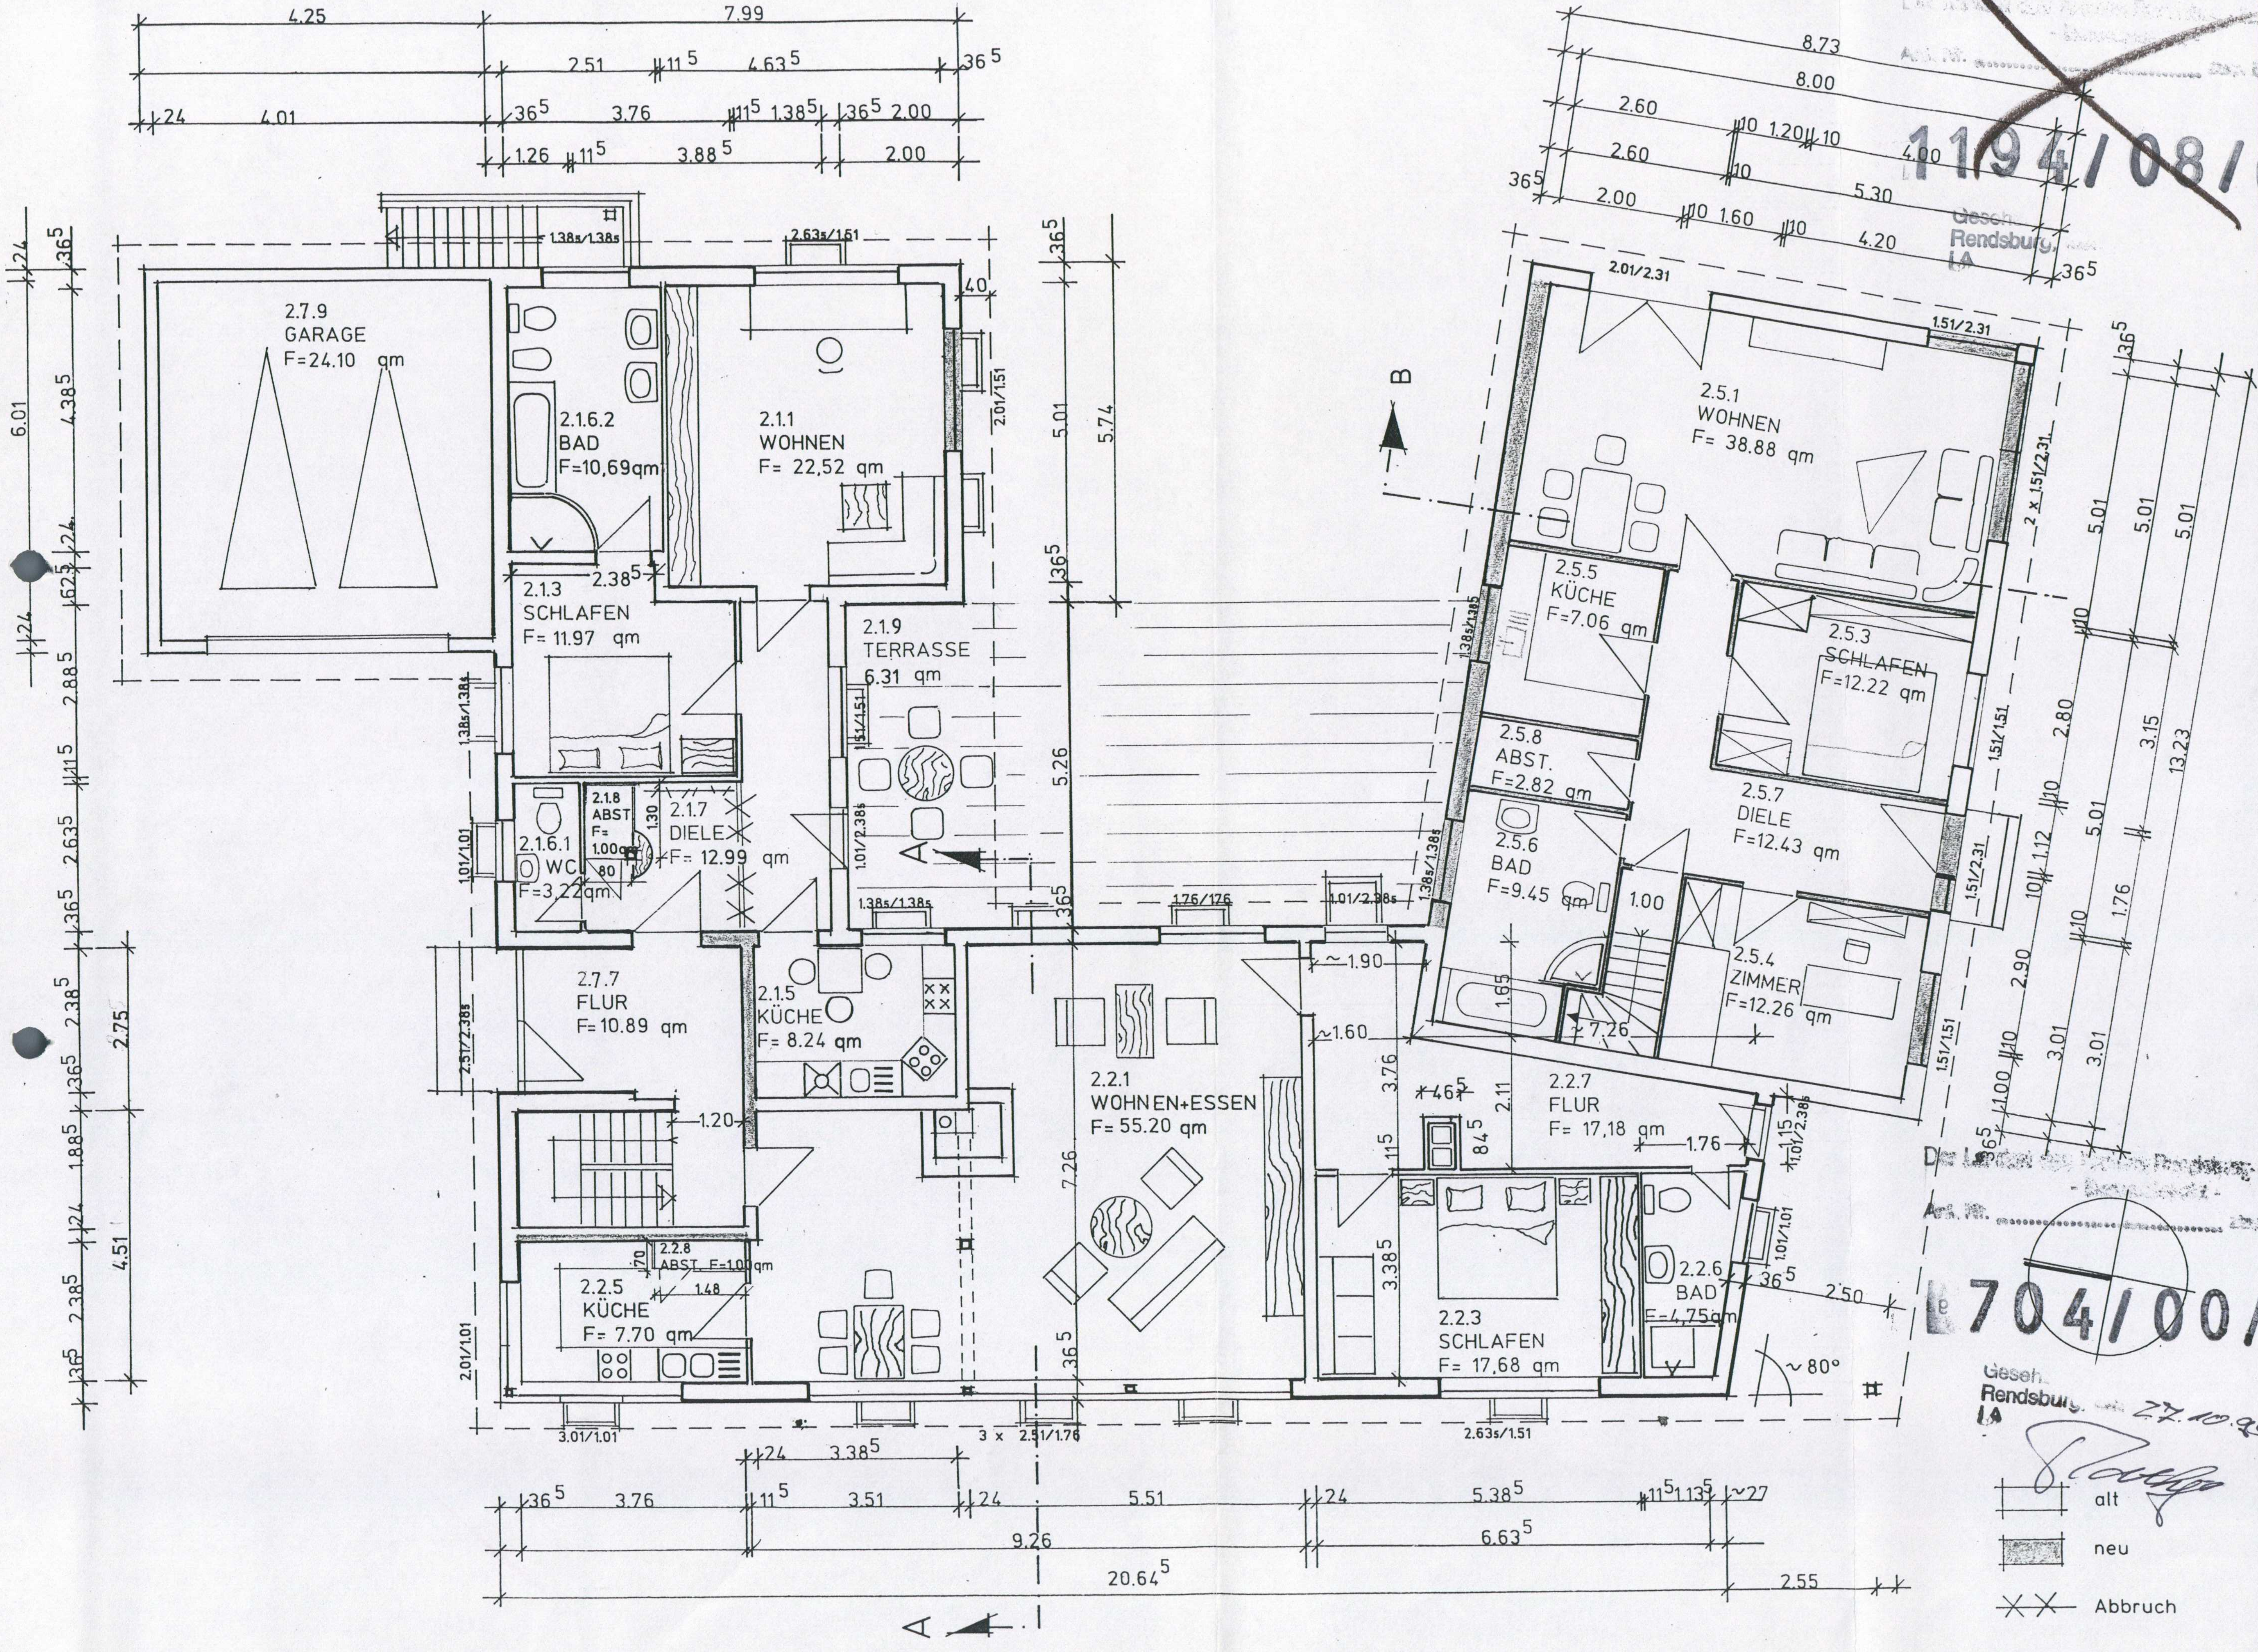
2.7.9 GARAGE F=24.10 qm
2.1.6.2 BAD F=10,69qm
2.1.1 WOHNEN F= 22,52 qm
2.1.3 SCHLAFEN F= 11.97 qm
2.1.9 TERRASSE 6.31 qm
2.1.6.1 WC F=3.22qm
2.1.8 ABST. F= 1.00qm
2.1.7 DIELE F= 12.99 qm
2.7.7 FLUR F= 10.89 qm
2.1.5 KÜCHE F= 8.24 qm
2.2.1 WOHNEN+ESSEN F= 55.20 qm
2.2.5 KÜCHE F= 7.70 qm
2.2.8 ABST. F=1.00qm
2.2.7 FLUR F= 17,18 qm
2.2.3 SCHLAFEN F= 17,68 qm
2.2.6 BAD F=4,75qm
2.5.1 WOHNEN F= 38.88 qm
2.5.5 KÜCHE F=7.06 qm
2.5.3 SCHLAFEN F=12.22 qm
2.5.8 ABST. F=2.82 qm
2.5.7 DIELE F=12.43 qm
2.5.6 BAD F=9.45 qm
2.5.4 ZIMMER F=12.26 qm
A
B
~80°
20.64⁵
alt
neu
Abbruch

1194/08/66

Gesch. Rendsburg, LA

Der Landrat des Kreises Rendsburg-Eckernförde

704/00/95

Gesch. Rendsburg, den 27.10.95

BAUNR. 816 | Z.NR. 3/2 | MA. 1: 100 | GEZ. AKa

DER BAUVORLAGEBERECHTIGTE :

EG GRUNDRISS

DAT. 14.06.95. | GEÄ.

BAUVORHABEN : Umbau Einfamilienhaus

BAUORT : Wilhelm - Stabestr. 4
24582 Wattenbek

BAUHERR : Rolf Schwarten & Siegfried Kleinert

DER BAUHERR: Schwarten

ENTWURF : PLANUNGSBÜRO DIETRICH LADWIG GMBH, 24582 BORDESHOLM, TEL. 04322 / 2264