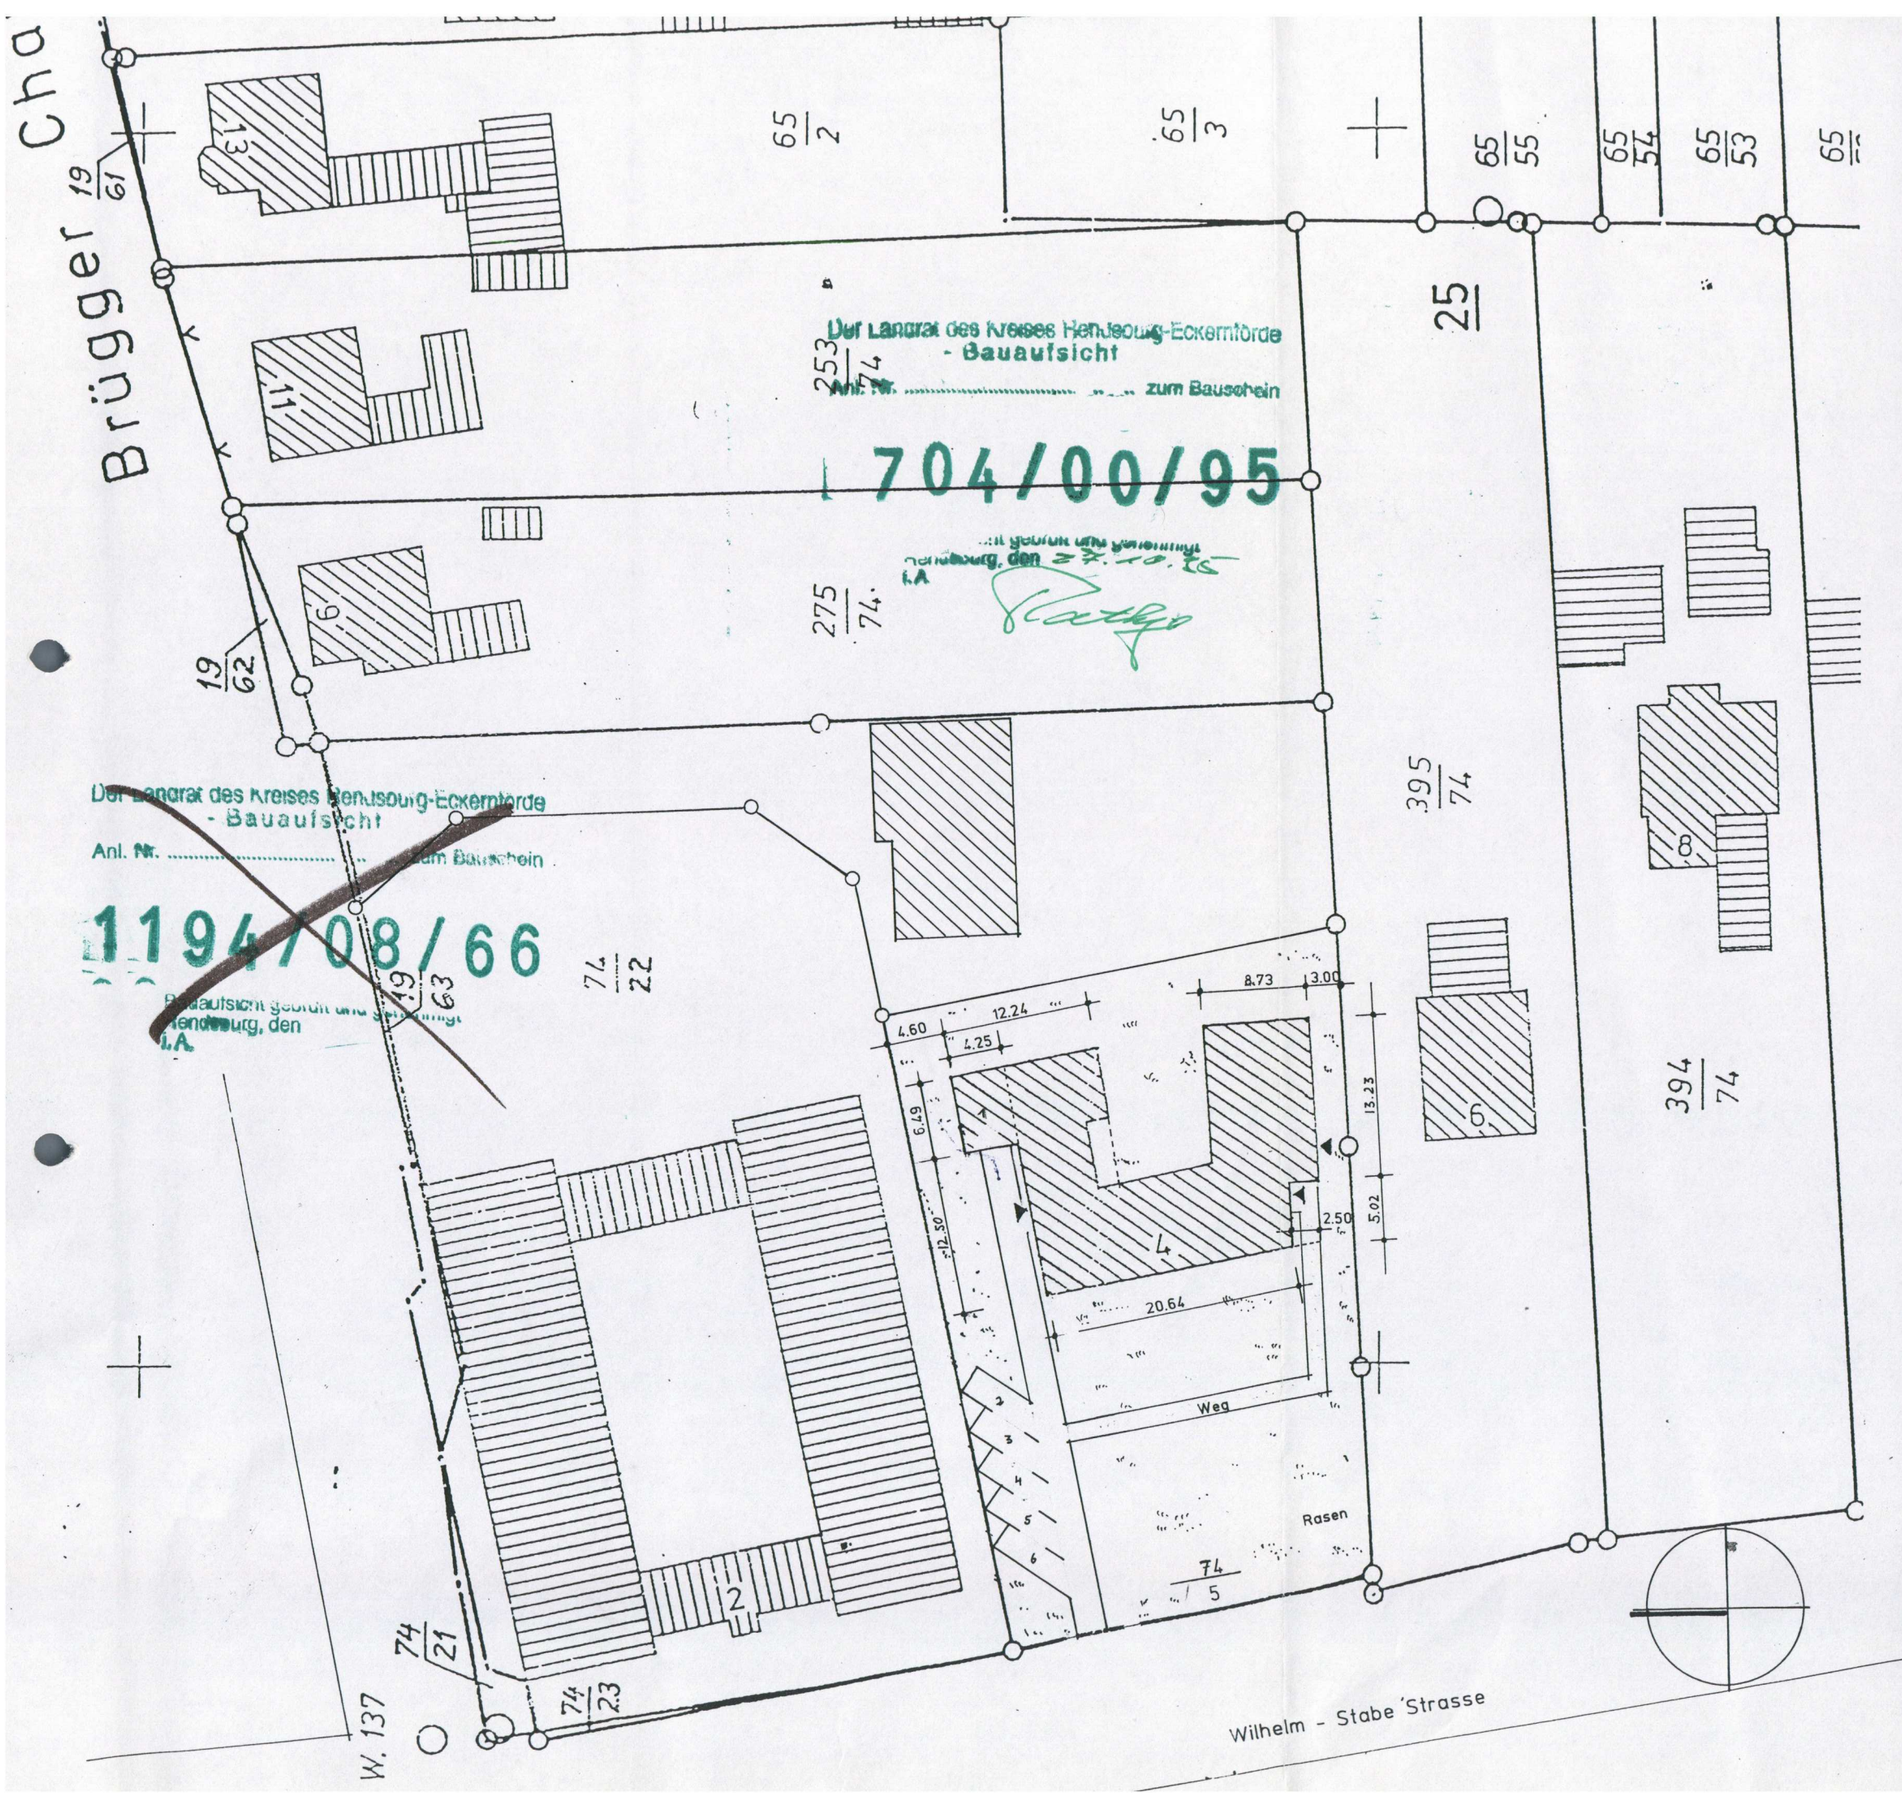


Lageplan nach §2 BauVorlVO vom 17.07.75

Angaben zum Baugrundstück

Kreis	:	Rendsburg - Eckernförde
Gemeinde	:	Wattenbek
Gemarkung	:	Wattenbek
Flur, Flurstück, Grösse (m²)	:	1
LB Nr.	:	
Grundbuch	:	
Eigentümer	:	Rolf Schwarten &
Jetzige Nutzung	:	Wohnhaus
Bemerkung	:	-

Festsetzungen für das Baugrundstück

Bebauungsplan Nr.	:	Nr. 10 ,1. Änderung , " Ortsmitte."
Art der baulichen Nutzung	:	Mischgebiet
Mass der baulichen Nutzung Z =		
GRZ =		0.2
GFZ =		0.3
Bauweise	:	offen/~~geschlossen~~

Berechnungen

Baugrundstück

Fläche des Baugrundstückes	:		m²
zu nach §21 BauNVO	:		m²
ab Fl. von der Strassenbegrenzungslinie	:		m²
ab Teilfläche, die nicht im Bauland liegen (§19 BauNVO)	:		m²
massgebende Grundstücksfläche MGF	:	1034	m²

Bauliche Anlagen

vorhandene Grundfläche	= GR vorh.	=	m²
geplante Grundfläche		=	m²
(Grundflächen nach §19 BauNVO)			
zukünftige Grundfläche	= GR	=	m²
zulässige Grundfläche	= GRZ *MGF	=	m²

vorhandene Geschossfläche	=	m²
Geplante Geschossfläche	=	m²
(Geschossflächen nach §20 BauNVO)		
zukünftige Geschossfläche	=	m²
zulässige Geschossfläche	=	m²

Mass der baulichen Nutzung

vorhandene GRZ = ———	= ———	=
zukünftige GRZ = ———	= ———	=
vorhandene GFZ = ———	= ———	=
zukünftige GFZ = ———	= ———	=

Legende

- vorh. öffentliche Verkehrsflächen
- festgesetzte, aber noch nicht vorhandene Verkehrsfläche
- geplante bauliche Anlagen
- vorhandene bauliche Anlagen
- zu beseitigende bauliche Anlagen
- Flächen, die von Baulasten betroffen sind
- Grenzen des Baugrundstücks
- Begrenzung von Abstandsflächen
- Baugrenze
- Baulinie
- I — Anzahl der Vollgeschosse
- +0.60 — Höhenlage über OK Strassenmitte
- EFH — Erdgeschossfussbodenhöhe
- 62/60 — Flurstück
- (5) — Hausnummer

Bauvorhaben :	Umbau Einfamilienhaus		
Bauort :	Wilhelm - Stabestr. 4 24582 Wattenbek		
Bauherr :	Rolf Schwarten & Siegfried Kleinert		
Der Bauherr :		Baunr. 816	Z.Nr. 3.0
		Lageplan	
Der Bauvorlageberechtigte :		M: 1:500	gez. R.D.L.
		Dat. 14.06.95	gepr.
		geä.	
Entwurf:	Planungsbüro Diedrich Ladwig GmbH, 24582 Bordesholm		