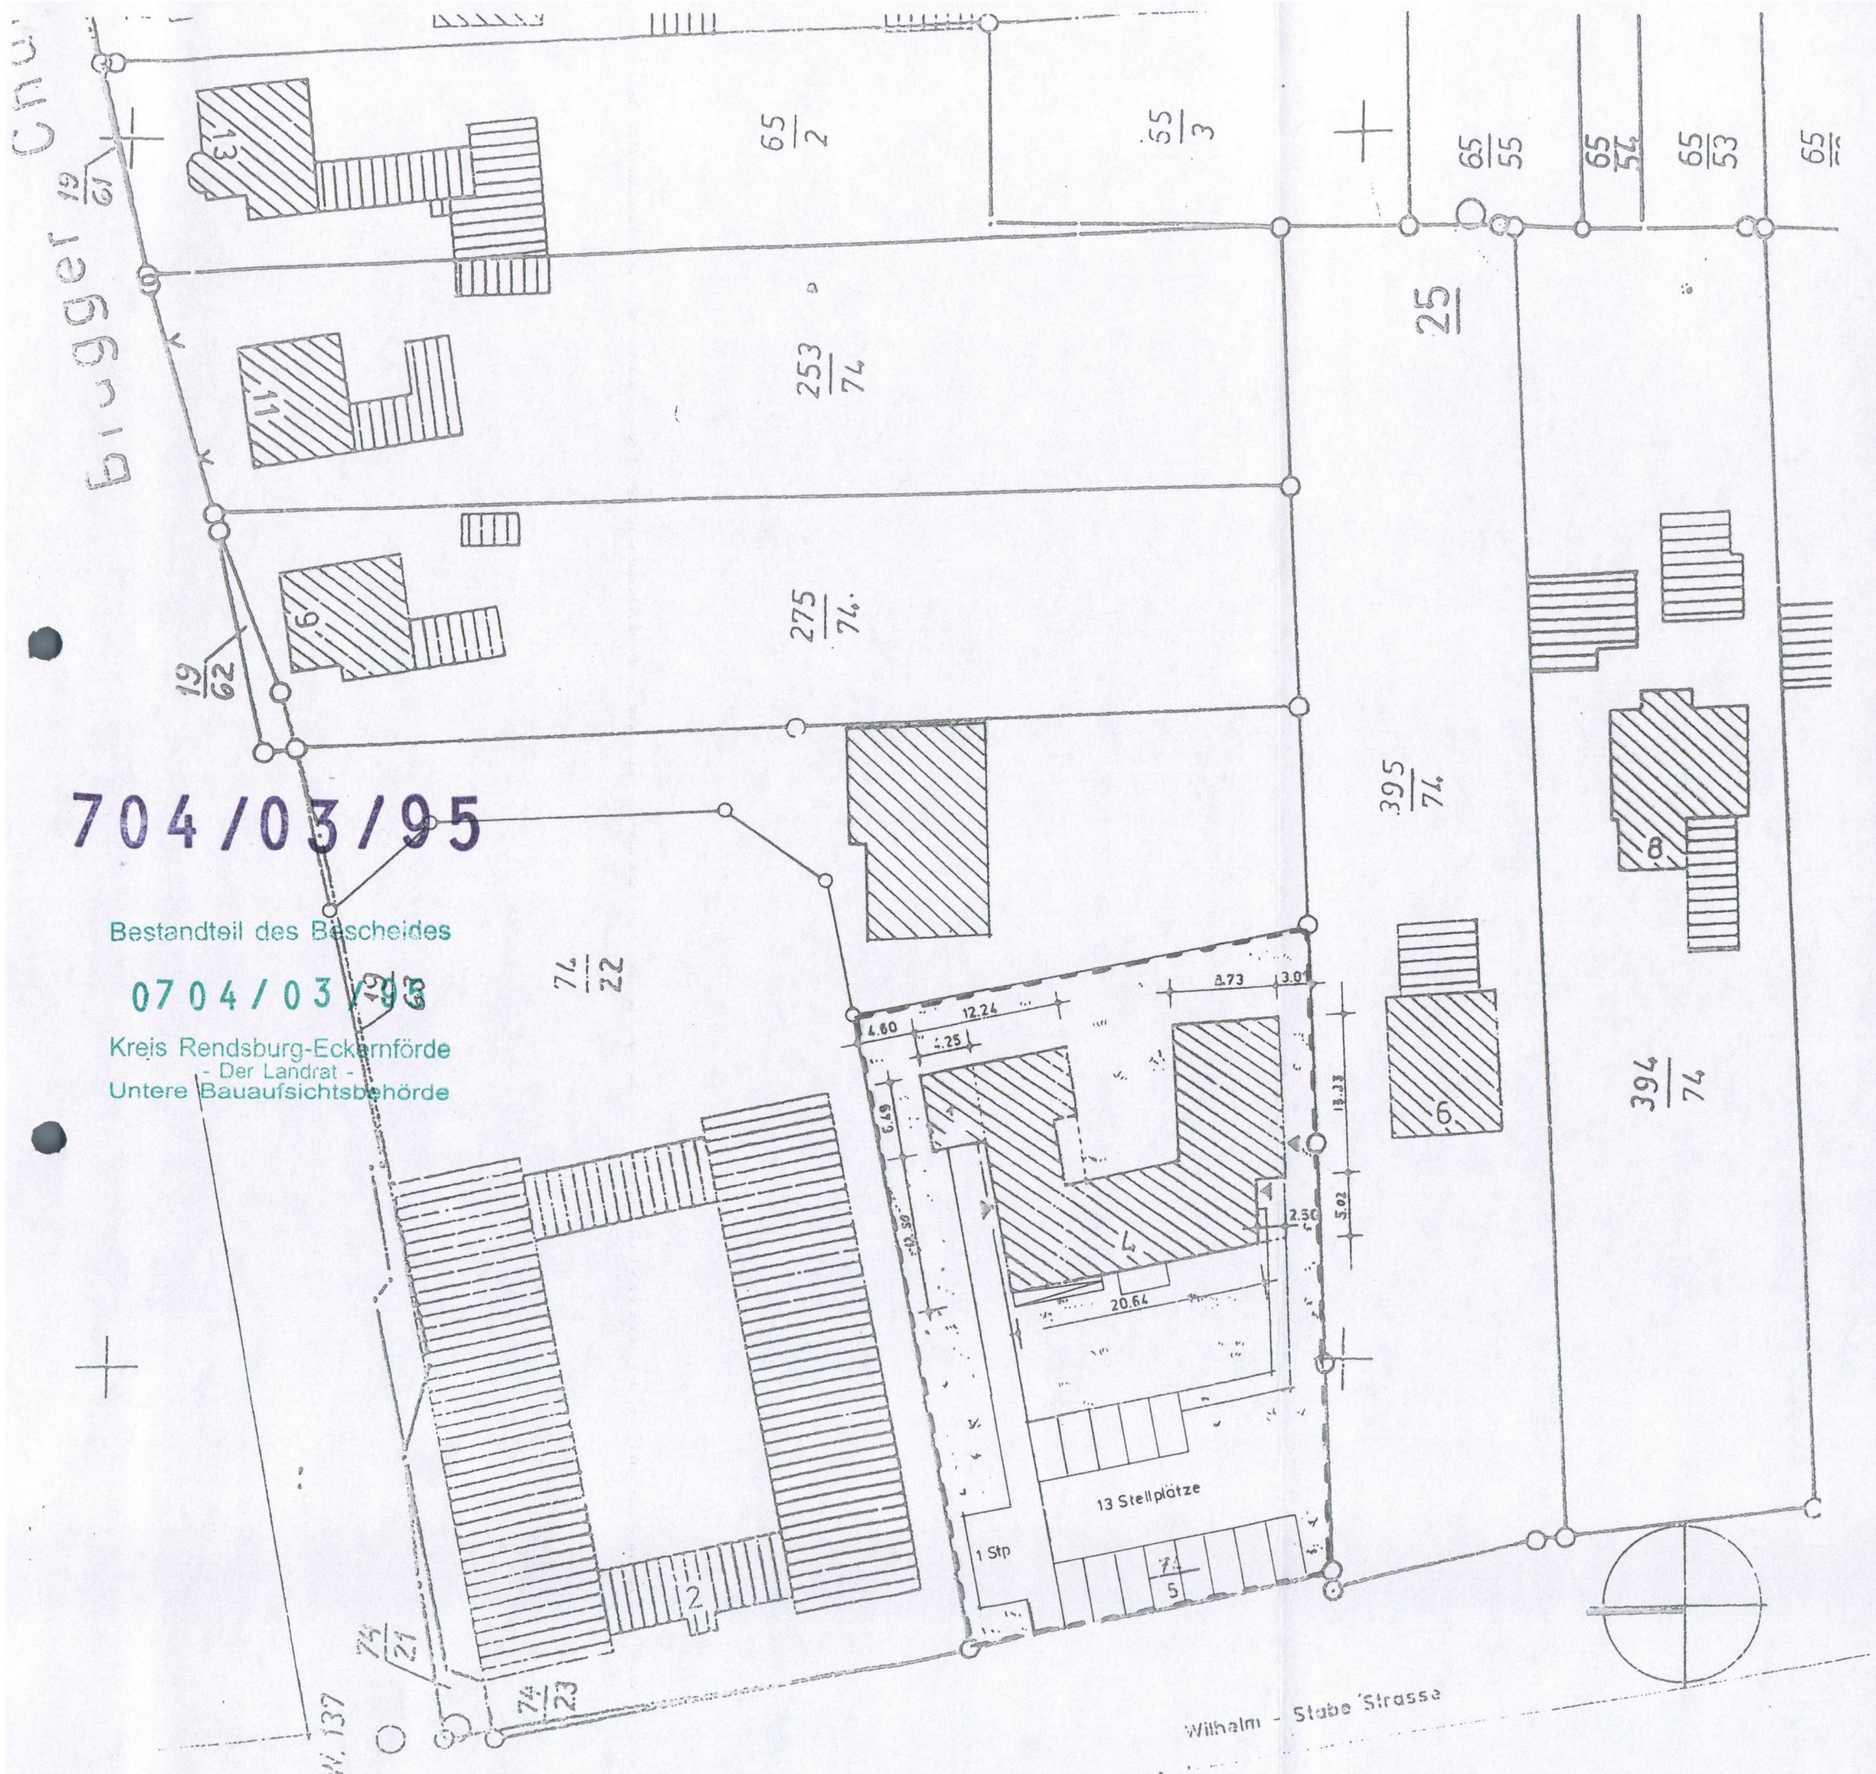



704/03/95

Bestandteil des Bescheides

0704/03/95

Kreis Rendsburg-Eckernförde
- Der Landrat -
Untere Bauaufsichtsbehörde

# Lageplan nach §2 BauVorlVO vom 17.07.75

## Angaben zum Baugrundstück

| | | |
|---|---|---|
| Kreis | : | Rendsburg - Eckernförde |
| Gemeinde | : | Wattenbek |
| Gemarkung | : | Wattenbek |
| Flur, Flurstück, Grösse (m²) | : | 1 |
| LB Nr. | : | |
| Grundbuch | : | |
| Eigentümer | : | Rolf Schwarten |
| jetzige Nutzung | : | Wohnhaus |
| Bemerkung | : | - |

## Festsetzungen für das Baugrundstück

| | | |
|---|---|---|
| Bebauungsplan Nr. | : | Nr. 10 ,1. Änderung , "Ortsmitte." |
| Art der baulichen Nutzung | : | Mischgebiet |
| Mass der baulichen Nutzung Z = | | |
| GRZ = 0.2 | | |
| GFZ = 0.3 | | |
| Bauweise | : | offen/geschlossen |

## Berechnungen

### Baugrundstück

| | | | |
|---|---|---|---|
| Fläche des Baugrundstückes | : | | 3333 m² |
| zu nach §21 BauNVO | : | | |
| ab Fl. von der Strassenbegrenzungslinie | : | | |
| ab Teilfläche, die nicht im Bauland | | | |
| liegen (§19 BauNVO) | : | | |
| massgebende Grundstücksfläche MGF | : | 1334 | 3333 m² |

### Bauliche Anlagen

| | | | |
|---|---|---|---|
| vorhandene Grundfläche | = GR vorh. | = | 333 m² |
| geplante Grundfläche | | = | 333 m² |
| (Grundflächen nach §19 BauNVO) | | | |
| zukünftige Grundfläche | = GR | = | 333 m² |
| zulässige Grundfläche | = GRZ * MGF | = | 333 m² |
| vorhandene Geschossfläche | | = | 333 m² |
| Geplante Geschossfläche | | = | 333 m² |
| (Geschossflächen nach §20 BauNVO) | | | |
| zukünftige Geschossfläche | | = | 333 m² |
| zulässige Geschossfläche | | = | 333 m² |

### Mass der baulichen Nutzung

| | | | |
|---|---|---|---|
| vorhandene GRZ = | ——— | = ——— | = |
| zukünftige GRZ = | ——— | = ——— | = |
| vorhandene GFZ = | ——— | = ——— | = |
| zukünftige GFZ = | ——— | = ——— | = |

## Legende

- vorh. öffentliche Verkehrsflächen
- festgesetzte, aber noch nicht vorhandene Verkehrsfläche
- geplante bauliche Anlagen
- vorhandene bauliche Anlagen
- zu beseitigende bauliche Anlagen
- Flächen, die von Bebauung betroffen sind
- Grenzen des Baugrundstücks
- Begrenzung von Abstandsflächen
- Baugrenze
- Baulinie
- I Anzahl der Vollgeschosse
- +0.60 Höhenlage über OK Strassenmitte
- EFH Erdgeschossfussbodenhöhe
- 74/22 Flurstück
- (4) Hausnummer

| | | |
|---|---|---|
| Bauvorhaben: Nutzungsänderung | | |
| Bauort : Wilhelm-Stabe-Str. 4, 24582 Wattenbek | | |
| Bauherr : Rolf Schwarten | | |
| Der Bauherr : Schwarten | Baunr.: 15 / 652 | Z.Nr.: 3/0 |
| | LAGEPLAN | |
| Der Bauvorlageberechtigte : Ludwig | M. 1:500 | gez. wie |
| | Dat. 11.09.2015 | gepr. |
| | geä. | |
| Architekturbüro Ralf Dieter Ludwig, Dipl.-Ing. | | |