Der [illegible] Eckernförde
- [illegible] -
Az. Nr. .... [illegible]

704/00/95

Geseh
Rendsburg,
i.A. 27.10.95

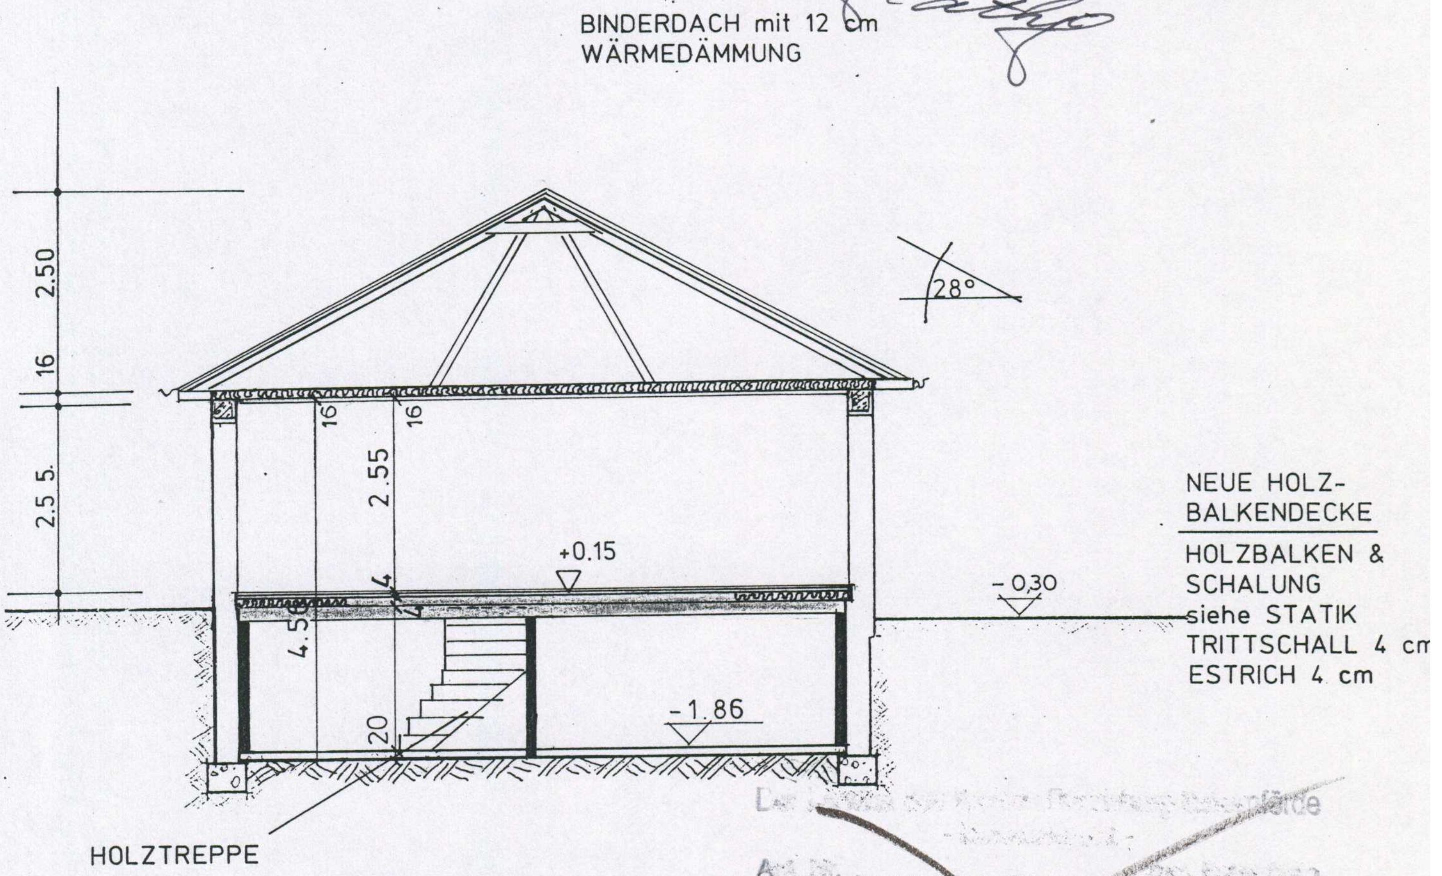

SCHNITT B-B SCHWIMMBAD

~~Der [illegible] Eckernförde~~
~~- [illegible] -~~
~~Az. Nr. .... [illegible]~~

~~1194/08/66~~

~~Gesehen~~
~~Rendsburg,~~
~~i.A.~~

▌ neues KS MAUERWERK

☐ alt

▨ neu

BAUVORHABEN:	UMBAU EINFAMILIENHAUS		
BAUORT :	WILHELM-STABE-STRASSE 4 WATTENBEK 24582	BAUNR. 816	Z.NR. 3/5
BAUHERR :	ROLF SCHWARTEN & SIEGFRIED KLEINERT	SCHNITT B-B	
DER BAUHERR : Schwarten	DER BAUVORLAGEBERECHTIGTE :	MA. 1:100	GEZ. AKa
		DAT. 14.06.95.	GEÄ.
ENTWURF : PLANUNGSBÜRO DIETRICH LADWIG GMBH 24582 BORDESHOLM, TEL. 04322 / 2264			