


WESTANSICHT

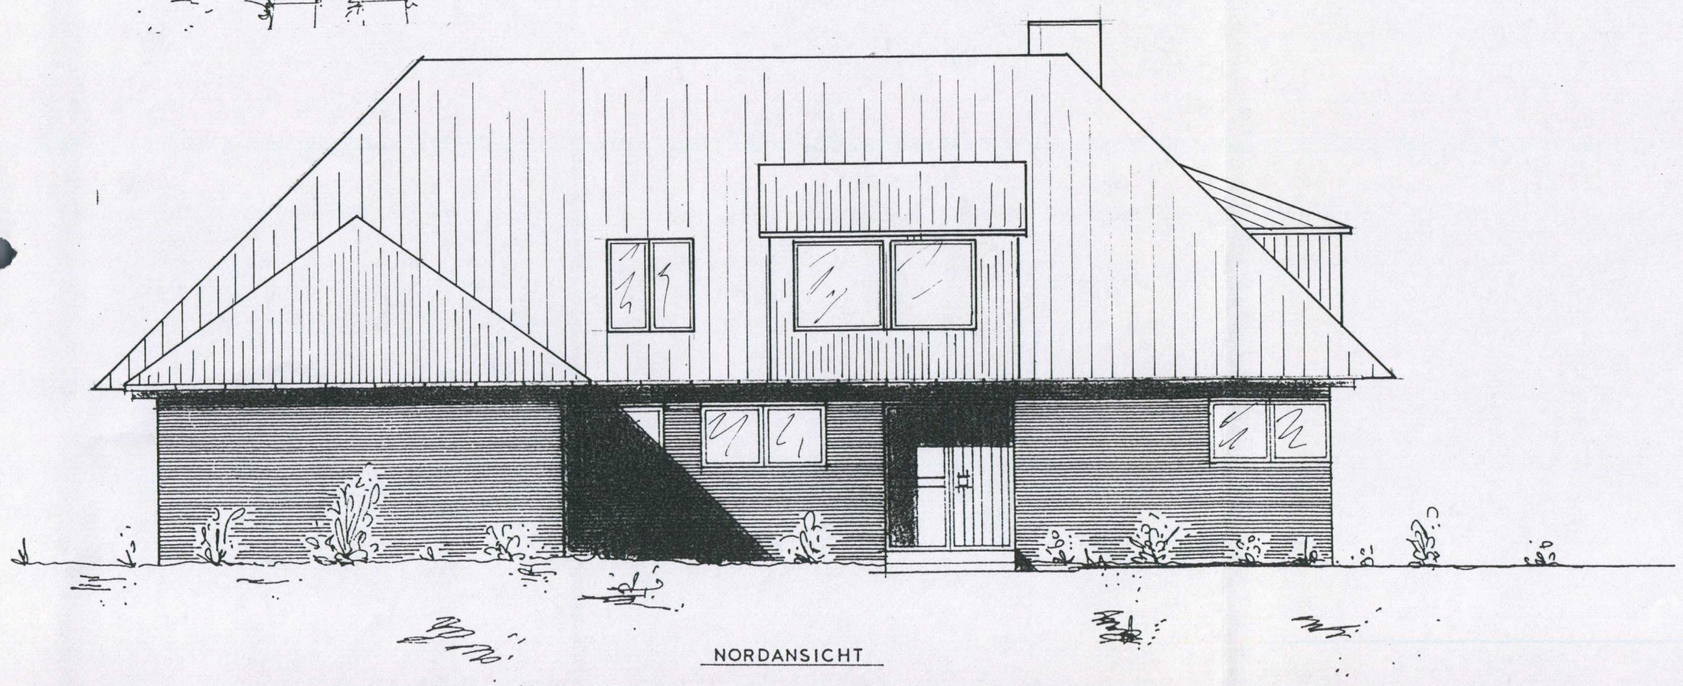

NORDANSICHT

Der Landrat des Kreises Rendsburg-Eckernförde
Amt für ...

704/00/95

Gesehen
Rendsburg, den 27.10.95
I.A.

Der Landrat des Kreises Rendsburg-Eckernförde
Amt für ...

1194/08/66

Gesehen
Rendsburg, den ...
I.A.

BAUVORHABEN: Umbau Einfamilienhaus
BAUORT : WATTENBEK / WILHELM-STABE-STRASSE
BAUHERR : ROLF SCHWARTEN & Siegfried Kleinert
ENTWURF : PLANUNGSBÜRO DIETRICH LADWIG GMBH. 24582 BORDESHOLM. TEL. 04322 / 2264

DER BAUHERR:

BAUNR. 816 | Z.NR. 3/6 | MA. 1:100 | GEZ. NO 5

DER BAUVORLAGEBERECHTIGTE:

ANSICHTEN

WESTANSICHT / NORDANSICHT

DAT. 14.06.95 | GEÄ.